


3D site titul

DESIGN PROJECT

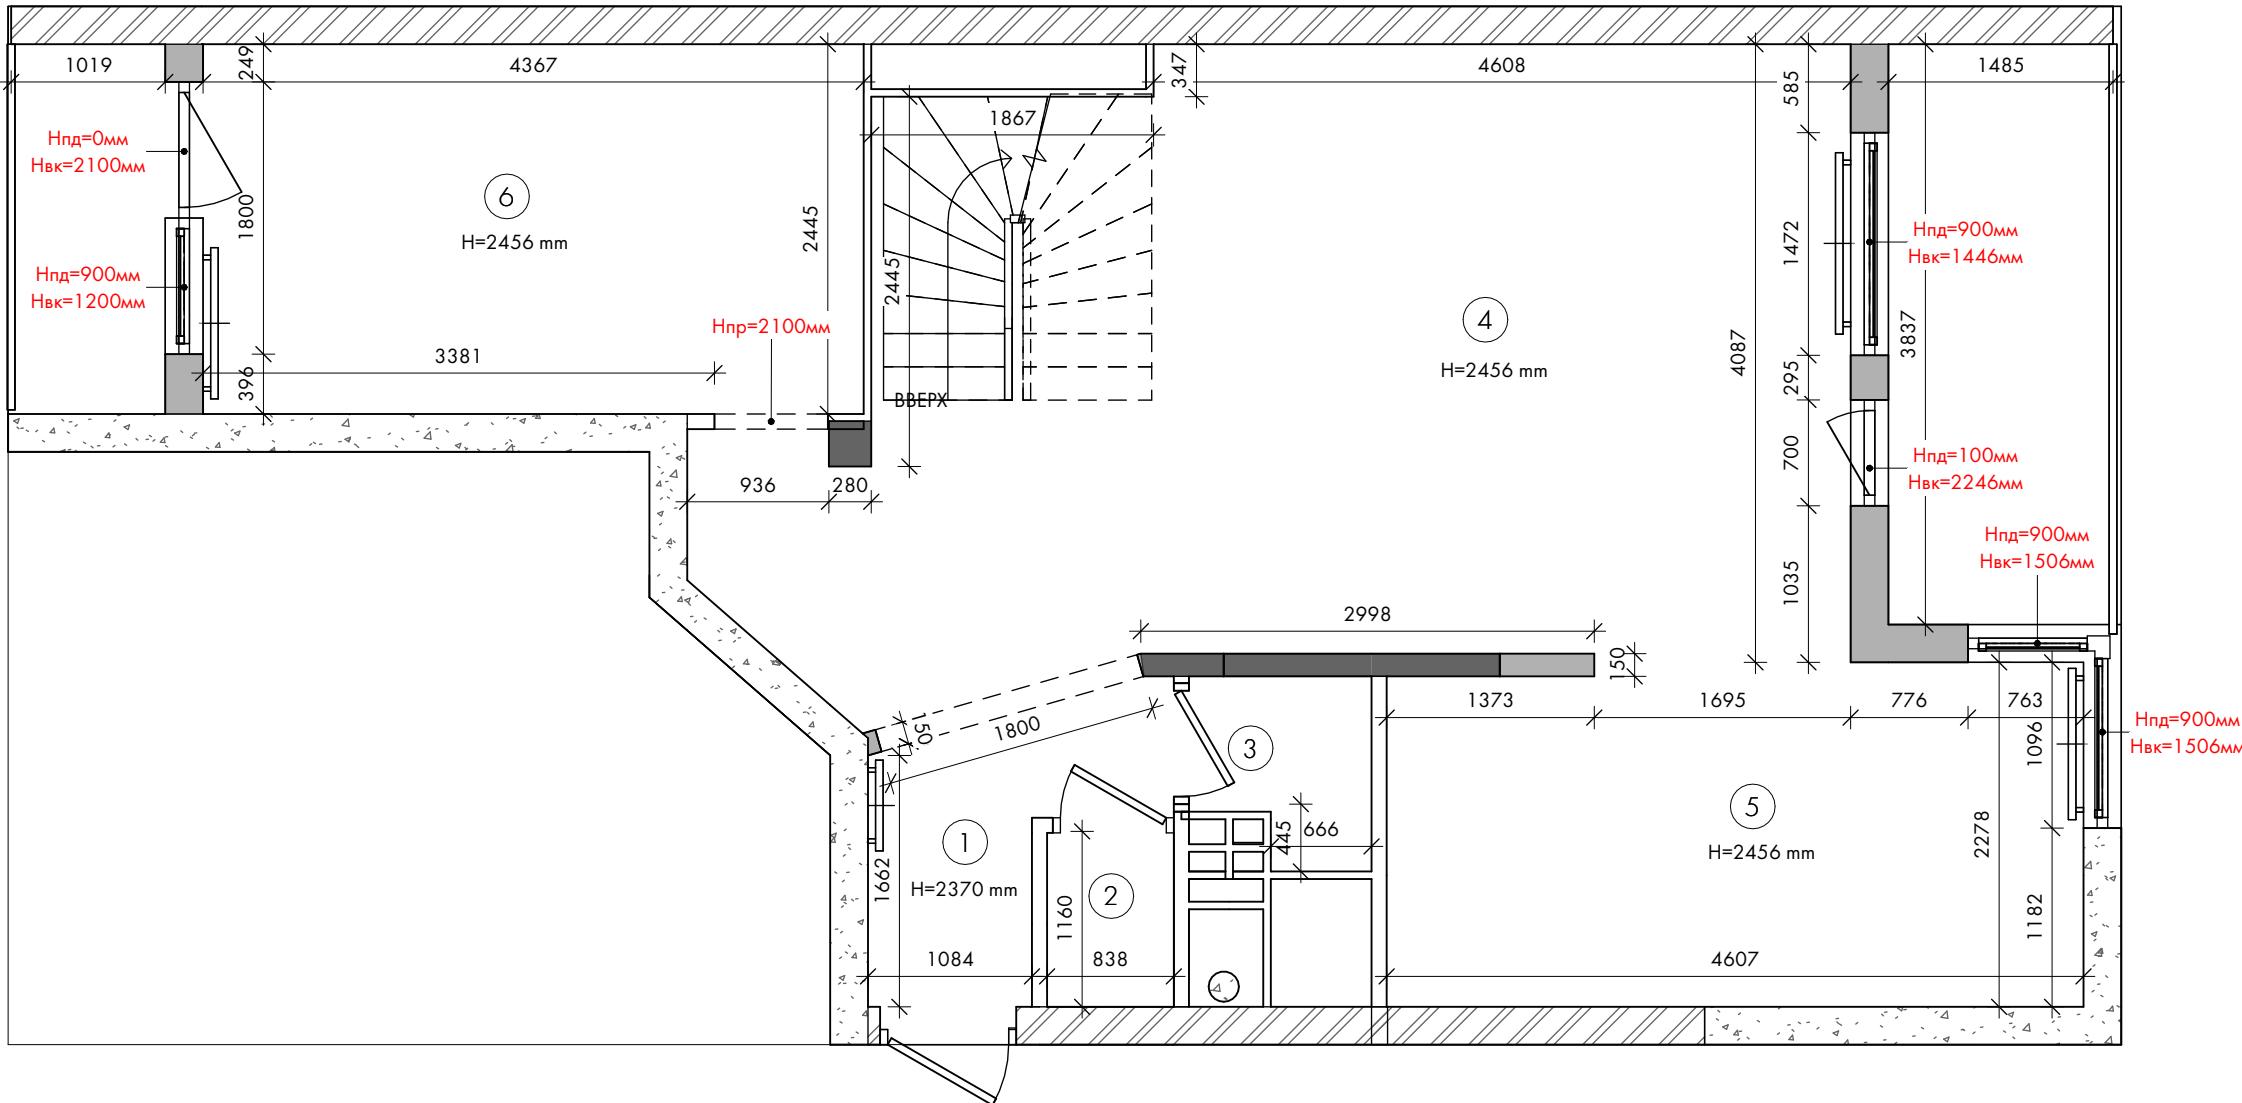


2. Plan pomiarowy

1 : 50

Назва проєкту: Apartment

Адреса проєкту:

Plan pomiarowy

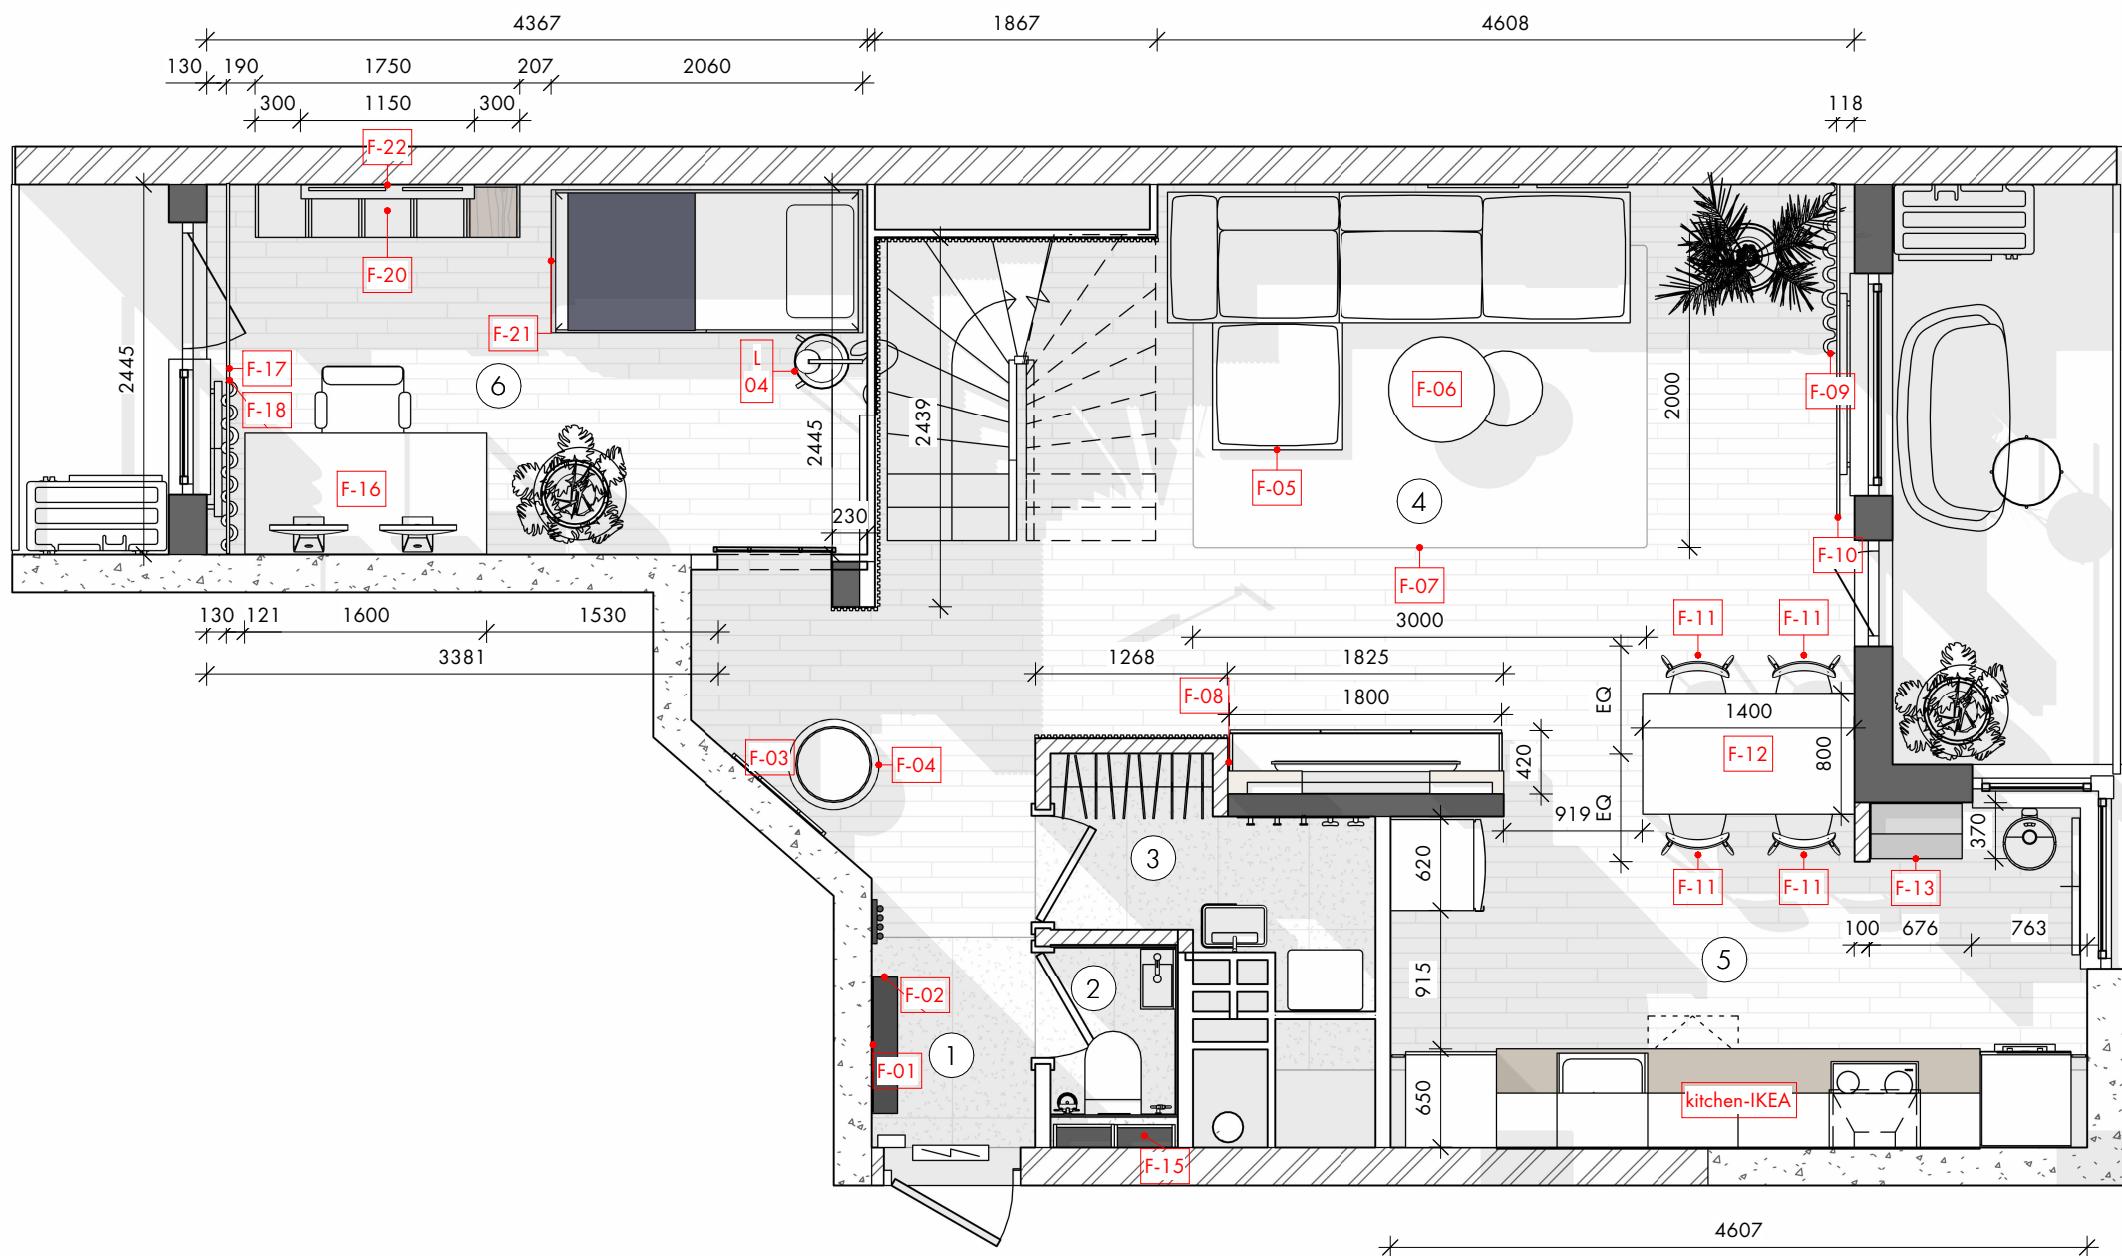


2. Uklad funkcjonalny

1 : 50


Название проекта:	Apartment
Адрес проекта:	

Уклад функциональный
S-01.2

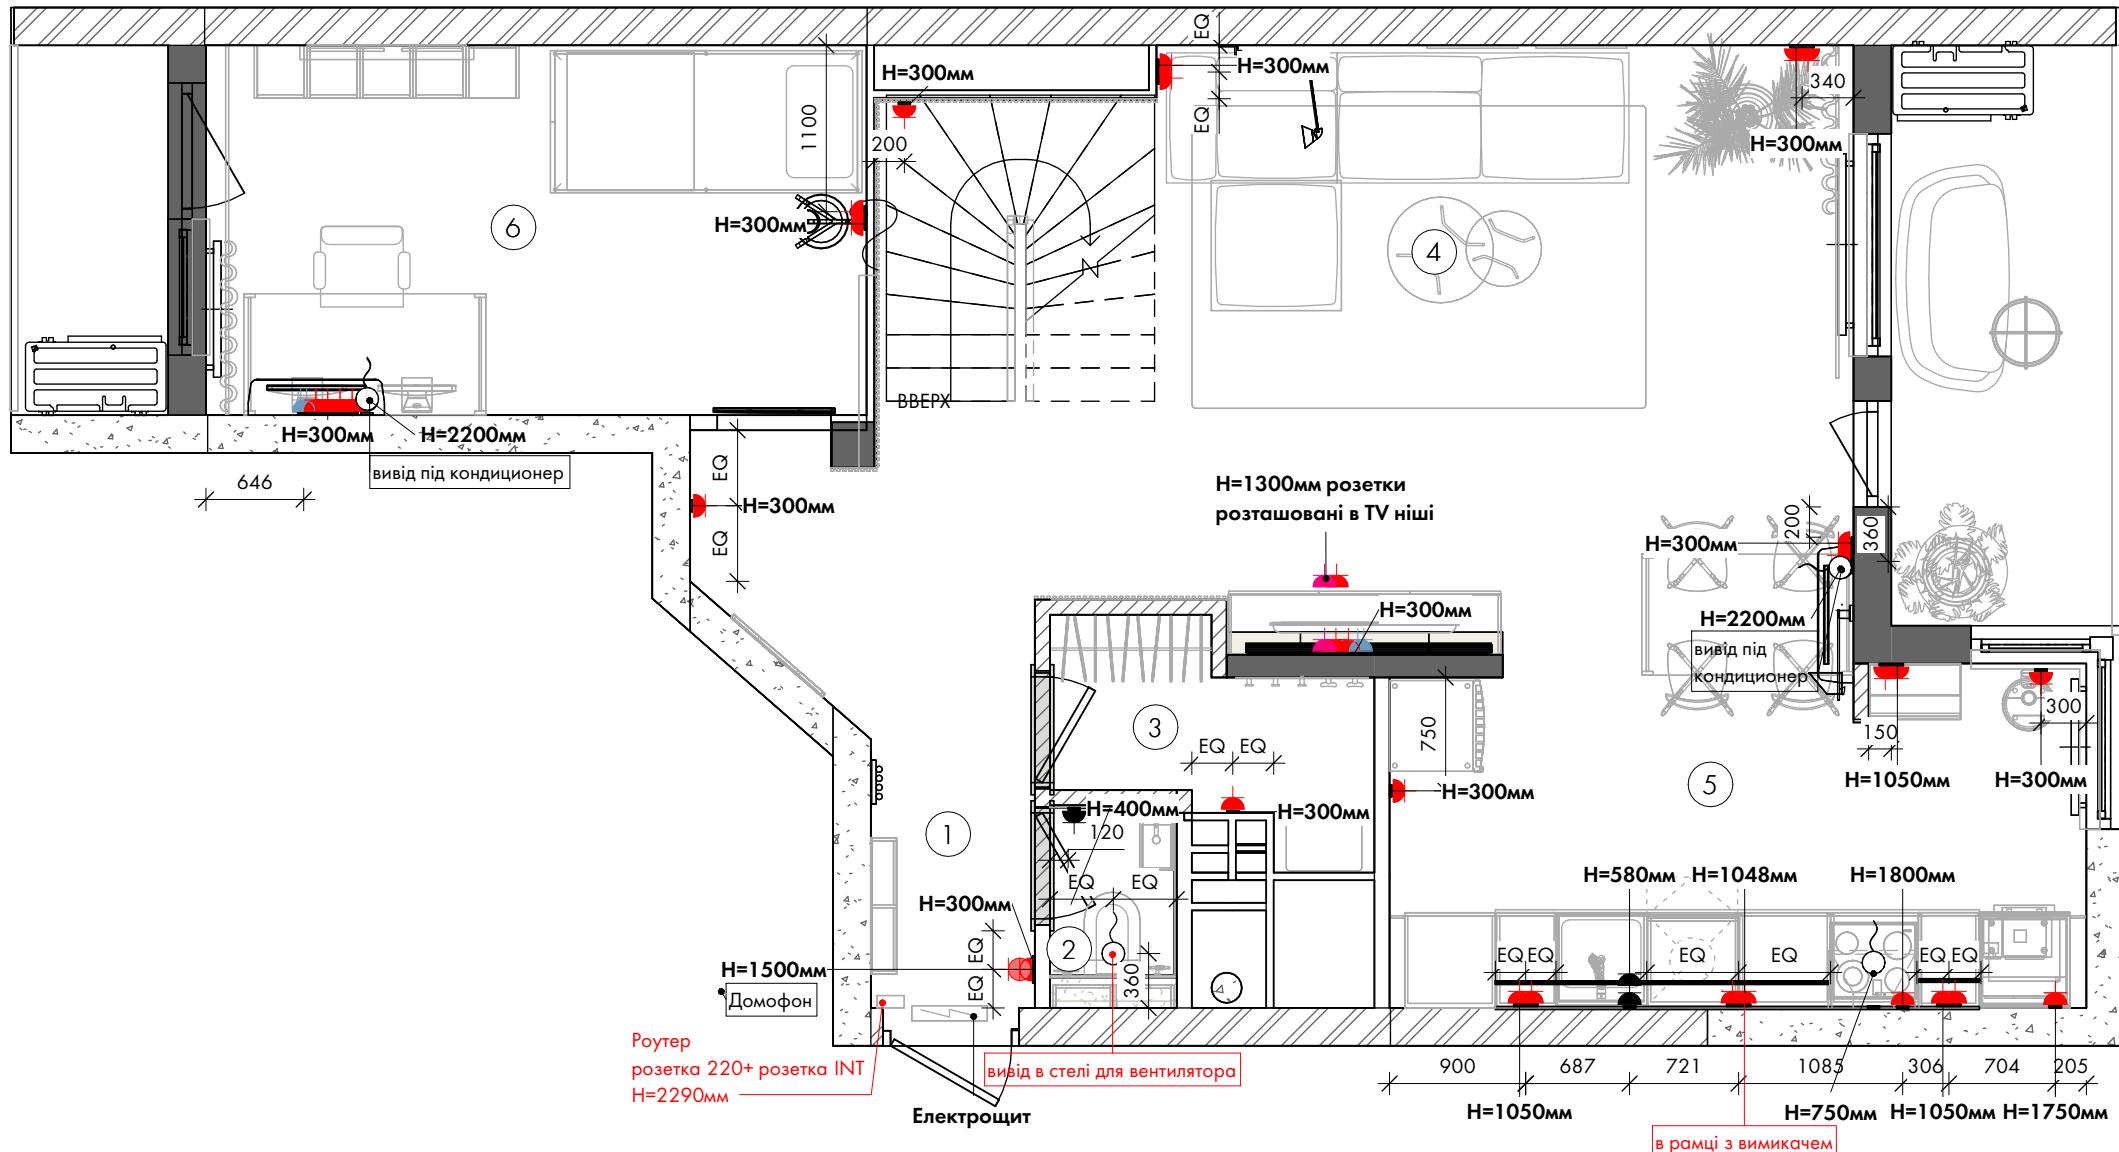

Назва проекту:	Apartment
Адреса проекту:	

Уклад розміщення пунктів електрических
S-02




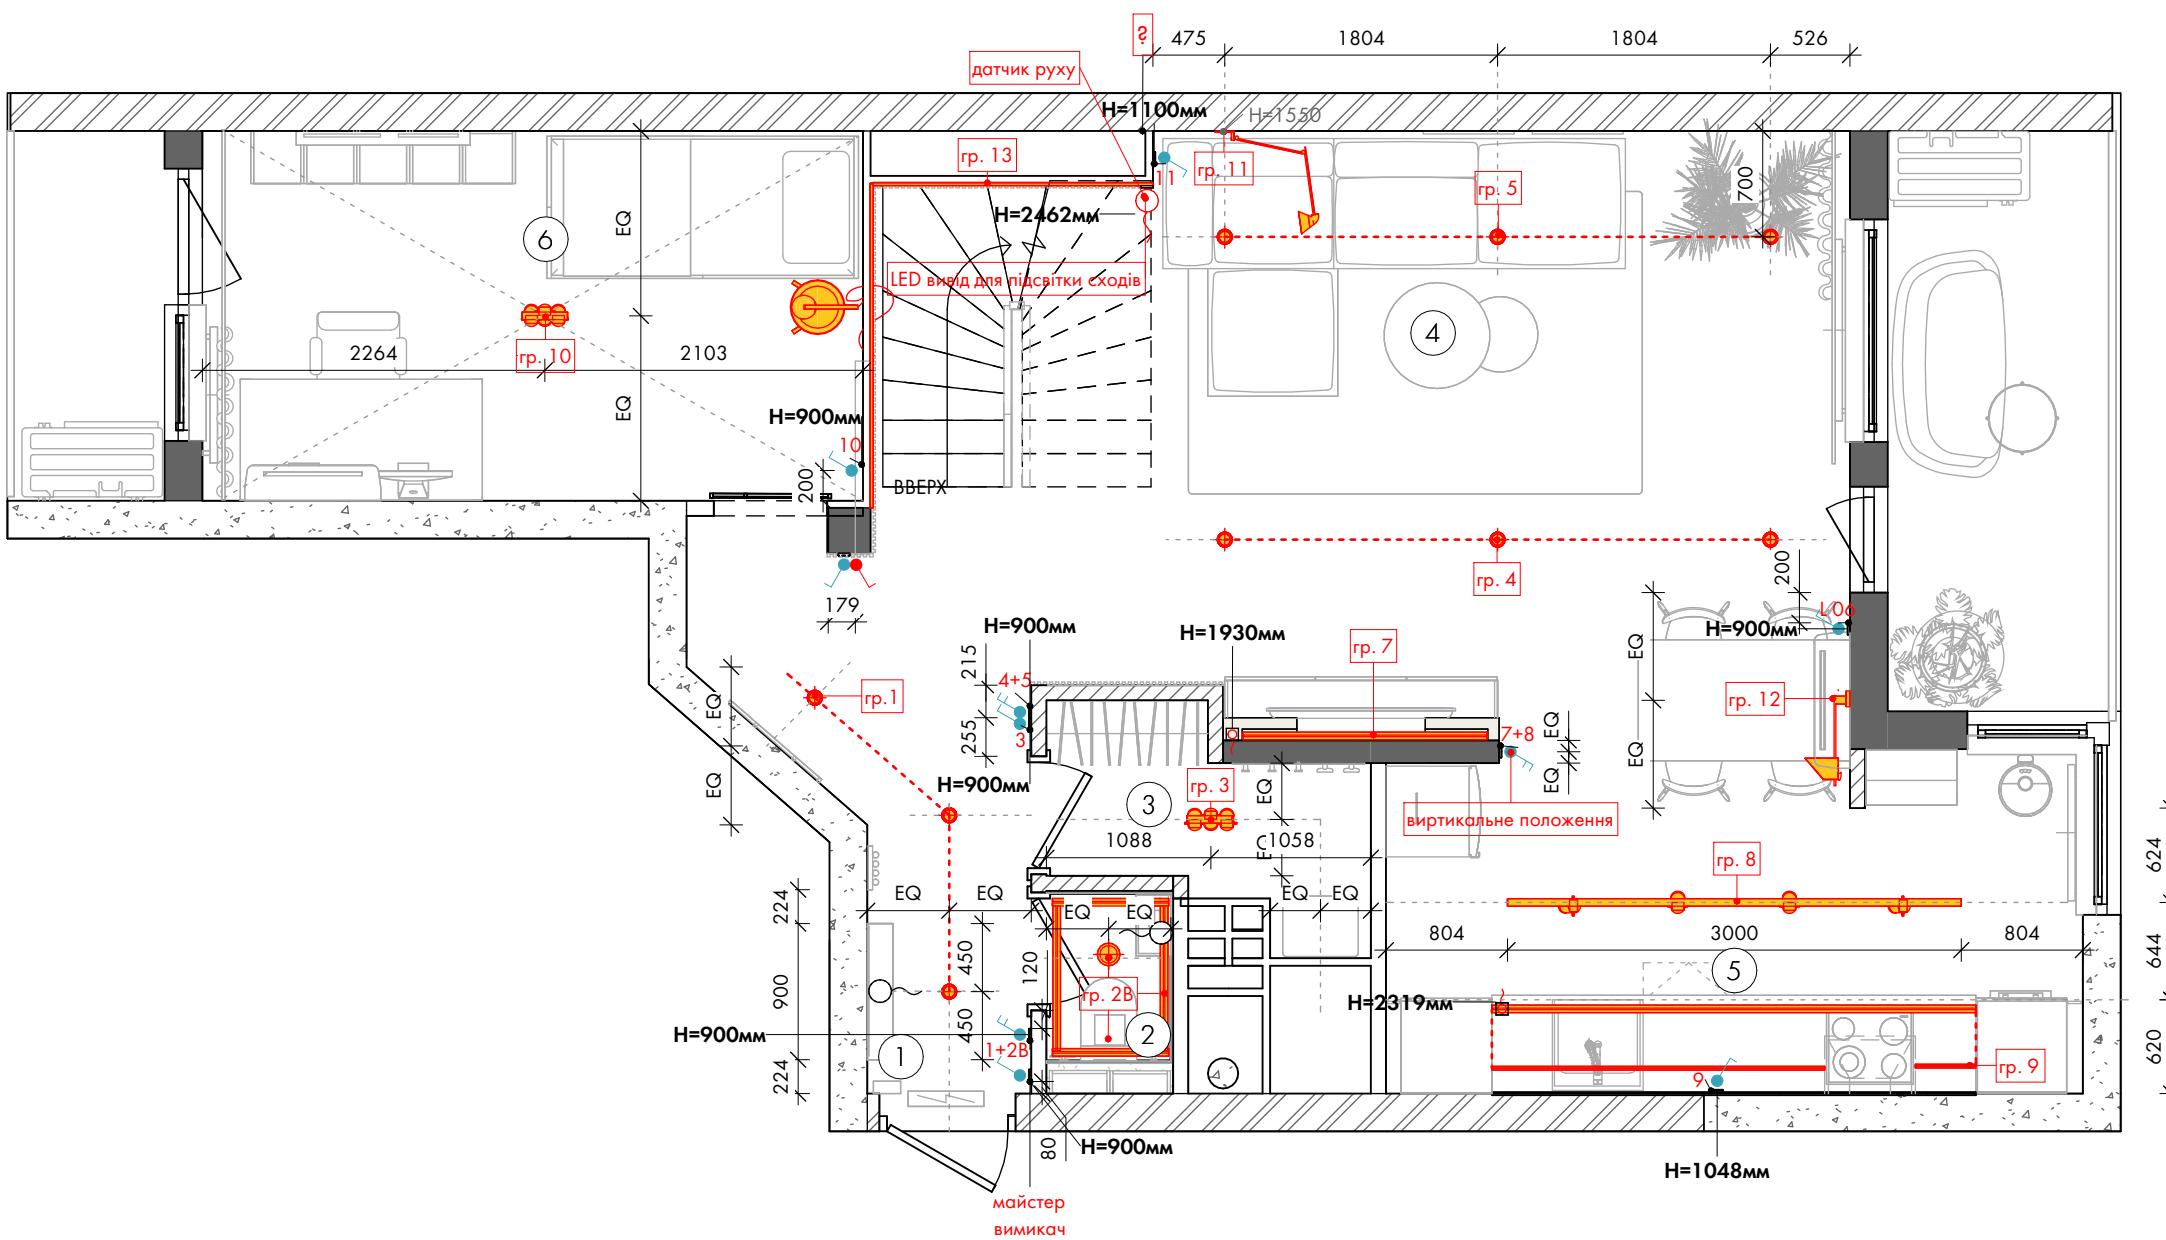


2. Układ rozmieszczenia opraw oświetleniowych

1 : 50

Назва проекту:	Apartment
Адреса проекту:	


Układ rozmieszczenia opraw oświetleniowych

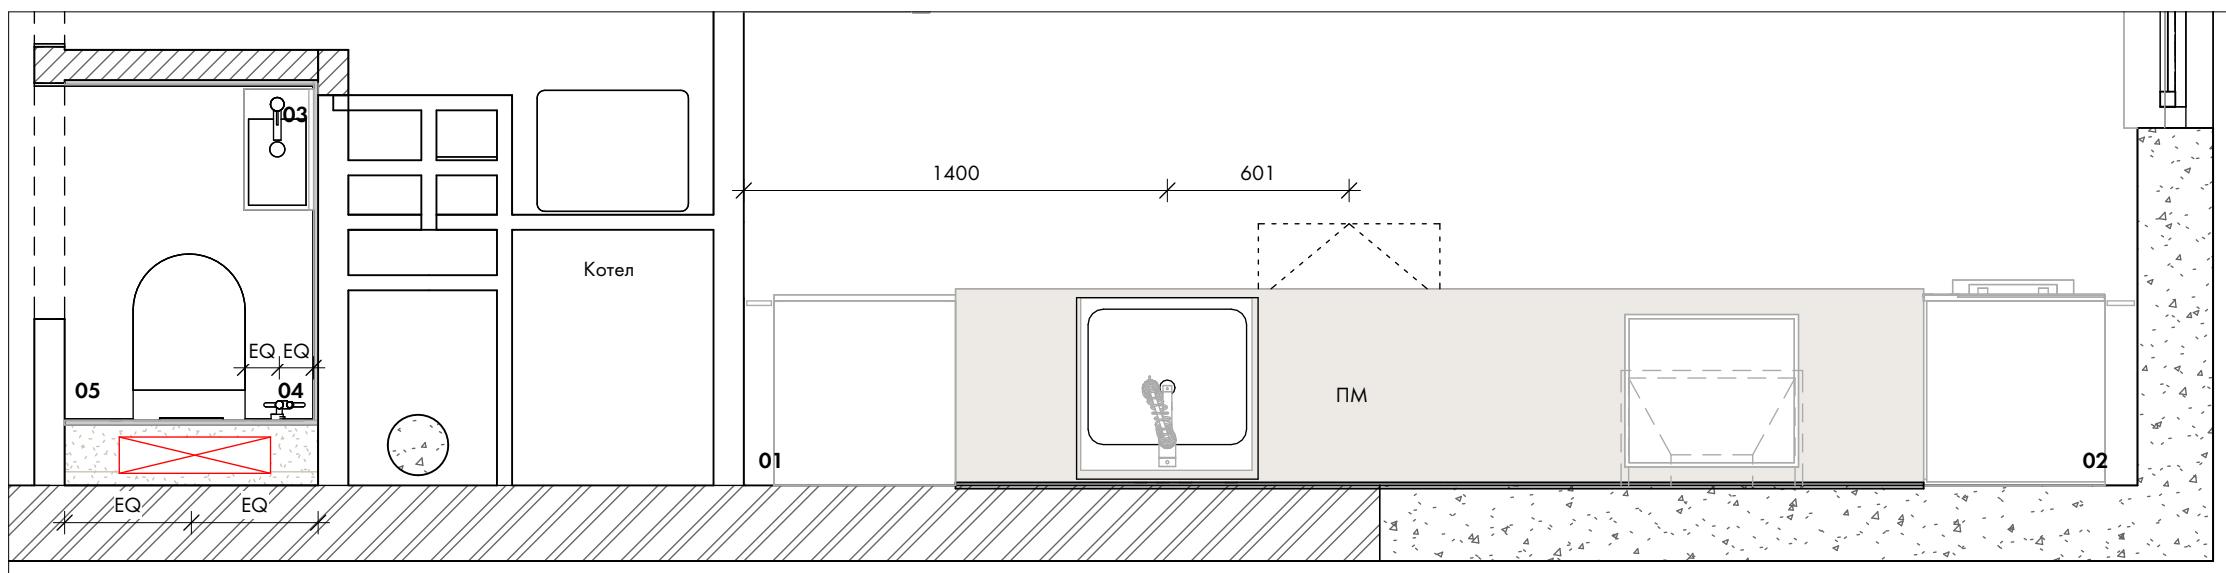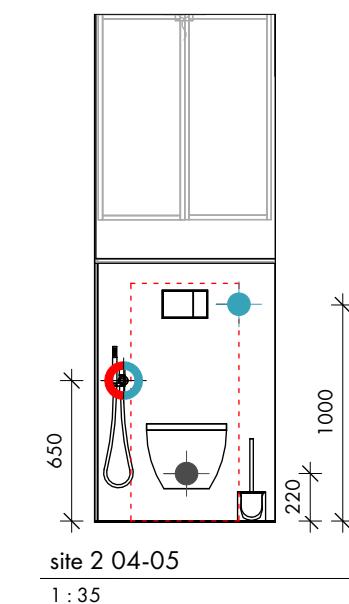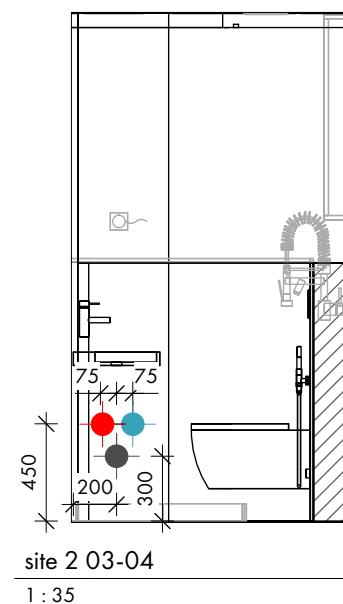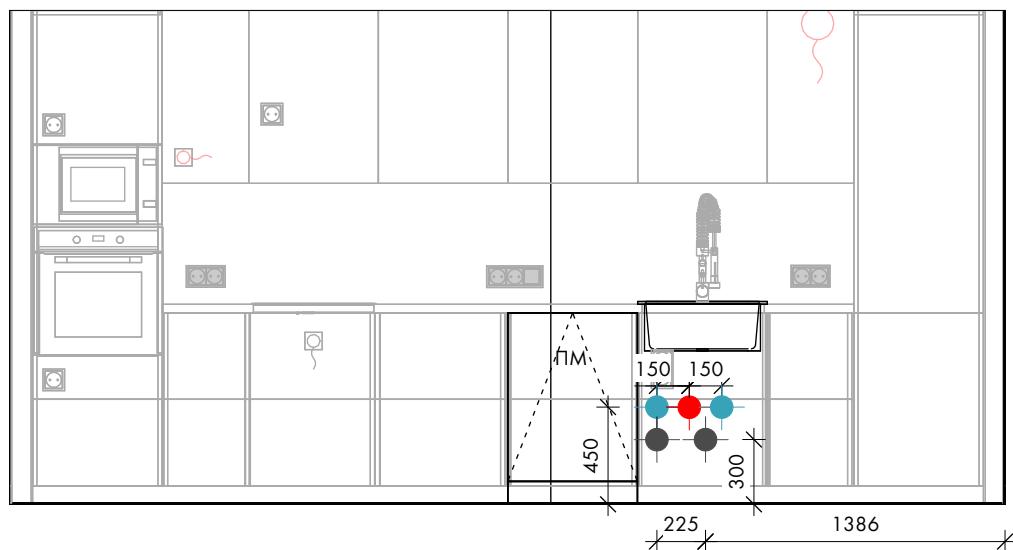

2. Уклад разміщення пунктів гідравлічних

Назва проекту:	Apartment
Адреса проекту:	


Уклад разміщення пунктів гідравлічних
S-03

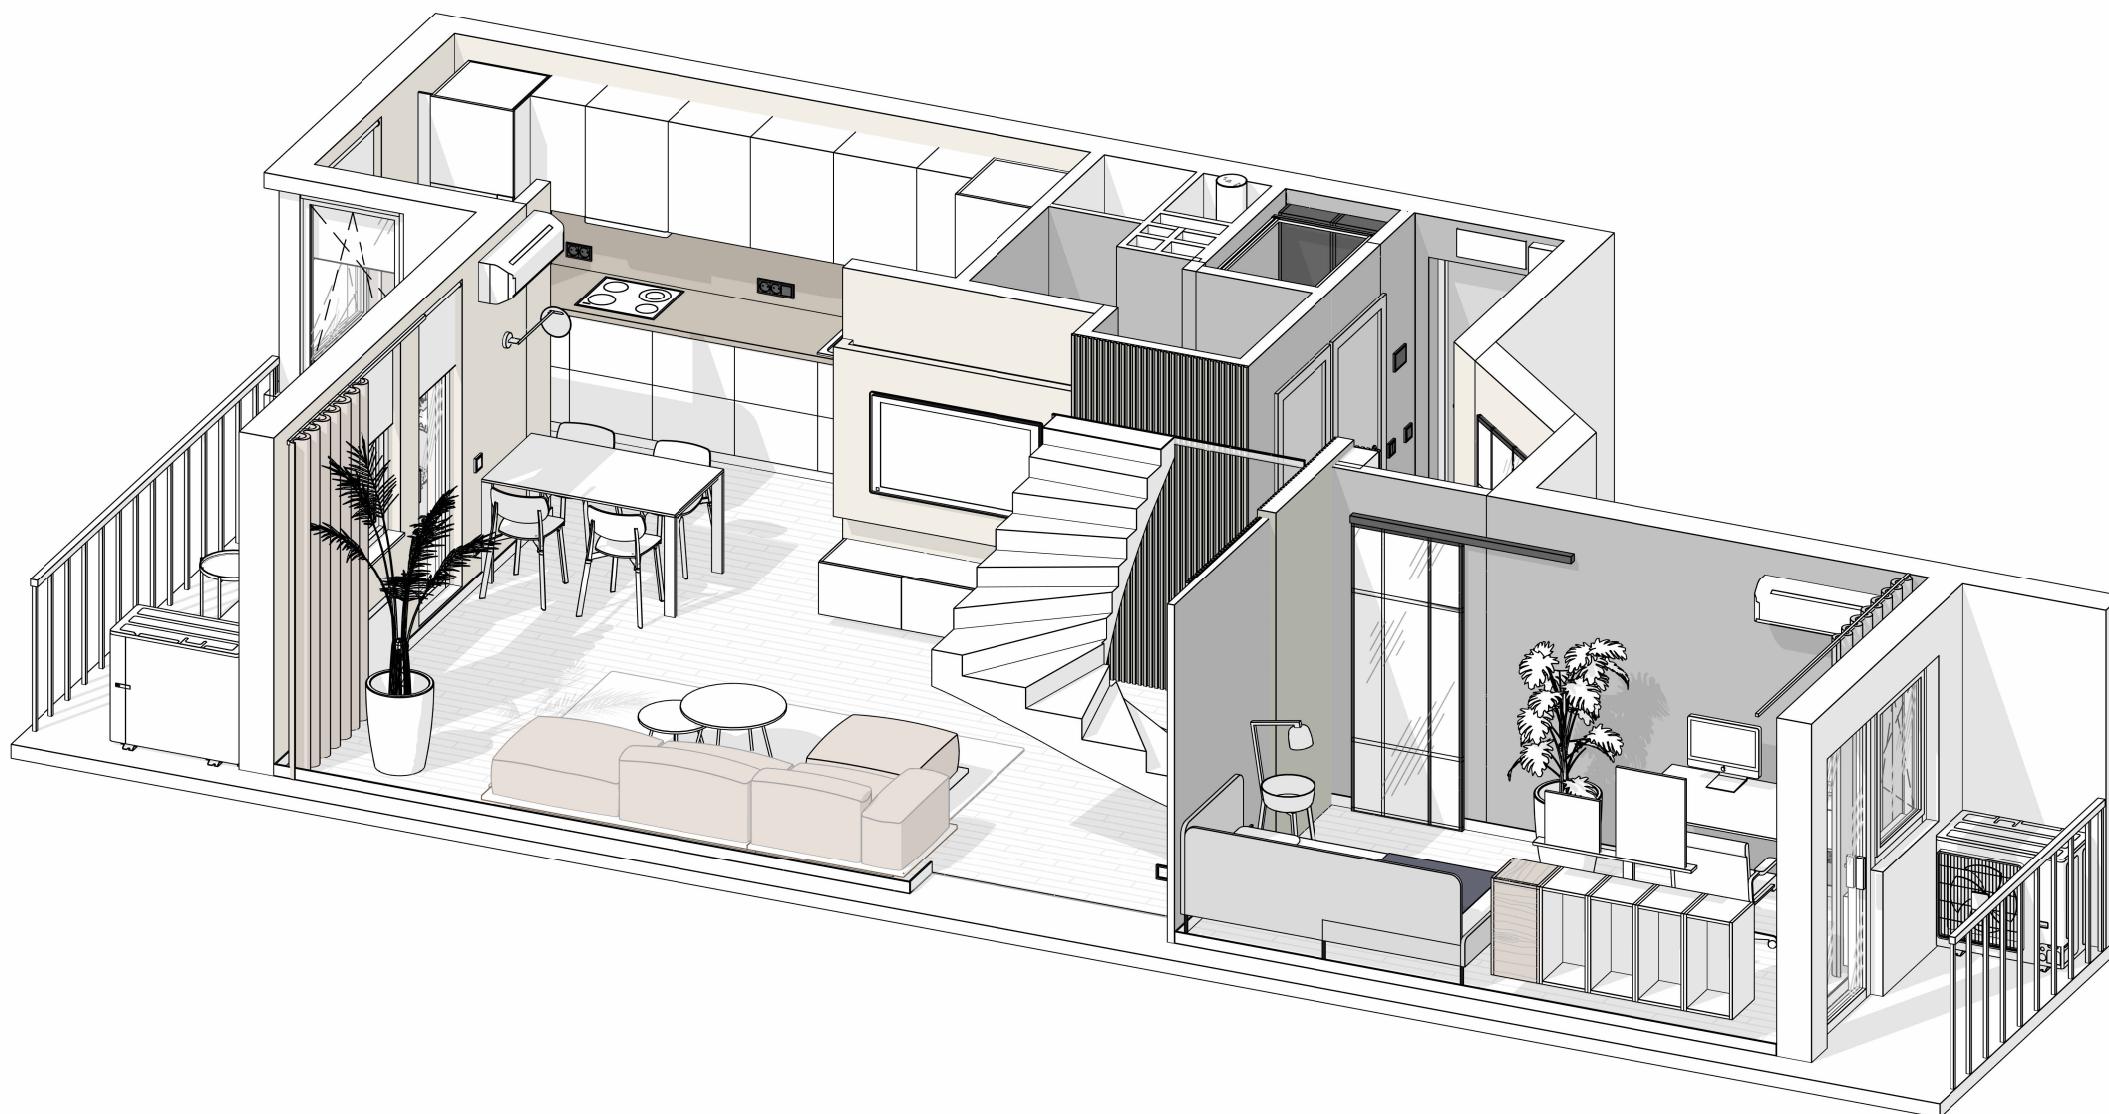

3D site 1 floor

Назва проекту:	Apartment
Адреса проекту:	

3D
S-04

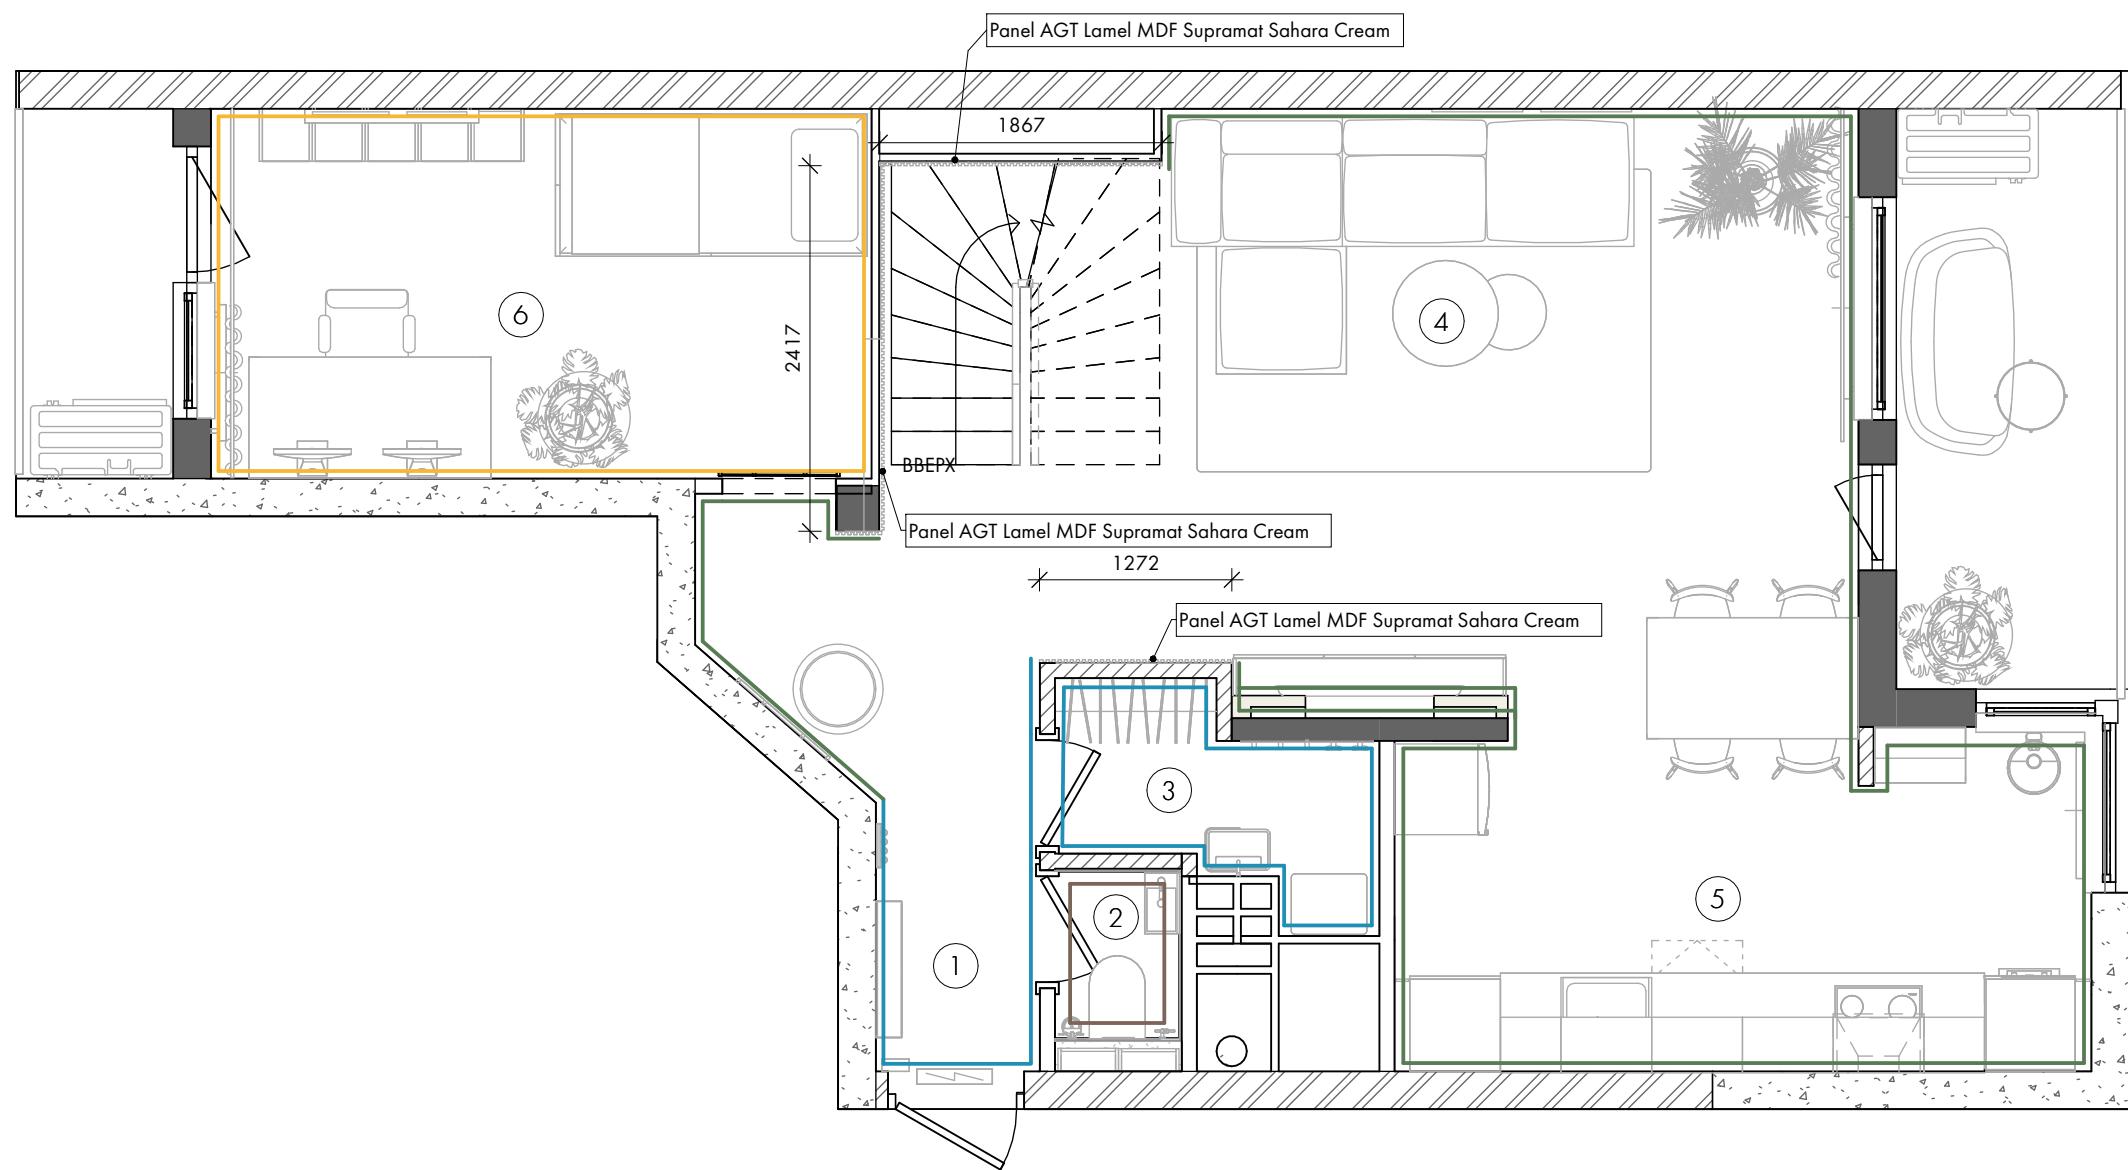

2. Plan materiałów

1 : 50

Lista materiałów

УП	№	Оздоблення	Площа
	ВФ 01	Вологостійне фарбування RAL 9003	19,43 м ²
	ВФ 02	Вологостійне фарбування NCS S 1502-Y502	5,42 м ²
	ДФ 01	Декоративне фарбування NCS S 1502-Y502	30,93 м ²
	ДФ 03	Декоративне фарбування NCS S 4502-B	28,42 м ²
	ДФ 04	Декоративне фарбування RAL 9010	102,06 м ²
	ДФ 06	Декоративне фарбування L4E W9E Freshwater Pearls	33,16 м ²
	ДФ 07	Декоративне фарбування RAL 070 70 10 taupe	33,24 м ²
	ДФ 08	Декоративне фарбування X 10 R22B Truffle Berry Cream	27,98 м ²
ПК 01		Плитка gres WILSON NATURAL 120x60 CARVING	3,51 м ²
ПК 02		Плитка SKY WALK WHITE MATT 60x120см	18,27 м ²

Panel AGT Lamel MDF Sahara Cream - 14.83 м.кв.

Назва проекту:	Apartment
Адреса проекту:	

Plan materiałów
S-05

LISTA MATERIAŁÓW

№	Матеріал	Зображення	Площа	Коефіцієнт	Площа	Примітки
ВФ 01	Вологостійне фарбування RAL 9003		26,42 м ²		0,00 м ²	
ВФ 02	Вологостійне фарбування NCS S 1502-Y502		6,45 м ²		0,00 м ²	
ДФ 01	Декоративне фарбування NCS S 1502-Y502		39,34 м ²		0,00 м ²	
ДФ 03	Декоративне фарбування NCS S 4502-B		28,42 м ²		0,00 м ²	
ДФ 04	Декоративне фарбування RAL 9010		182,42 м ²		0,00 м ²	
ДФ 05	Декоративне фарбування біла фарба +домішок стінової		111,10 м ²		0,00 м ²	
ДФ 06	Декоративне фарбування L4E W9E Freshwater Pearls		33,16 м ²		0,00 м ²	
ДФ 07	Декоративне фарбування RAL 070 70 10 taupe		60,98 м ²		0,00 м ²	
ДФ 08	Декоративне фарбування X 10 R22B Truffle Berry Cream		27,98 м ²		0,00 м ²	реальна площа панелей біля 15 м.кв.
НП-01	Настінні панелі AGT MDF SAHARA CREAM		41,66 м ²		0,00 м ²	
ПД-01	Ламінат		106,90 м ²		0,00 м ²	при замовлені треба додати 10-15%
ПК 01	Плитка gres WILSON NATURAL 120x60 CARVING		18,00 м ²		0,00 м ²	при замовлені треба орієнтуватися на кількість плиток, а не метраж
ПК 02	Плитка SKY WALK WHITE MATT 60x120см		111,55 м ²		0,00 м ²	

Назва проекту: Apartment

Адреса проекту:

Lista materiałów

S-06

Lista hydrauliczna

Марка	Фабрика, назва	Зображення	Кількість
	<варіанти>		39
01	Elita szafka z umywalką Young Basic 40 1D Black Matt PDW RE168996007160		1
02	гігієнічний душ		2
03	Zestaw WC Stelaż GROHE		2
04	Zlewozmywak FRANKE Sirius S2D 611-78 143.0612.630 Kamienny szary +Bateria FRANKE Lina 115.0626.085 Chrom/czarny		1
05	ПМ		1
06	Котел		1

Назва проекту:	Apartment
Адреса проекту:	

Lista hydrauliczna
S-07







